


PROJECT - 2

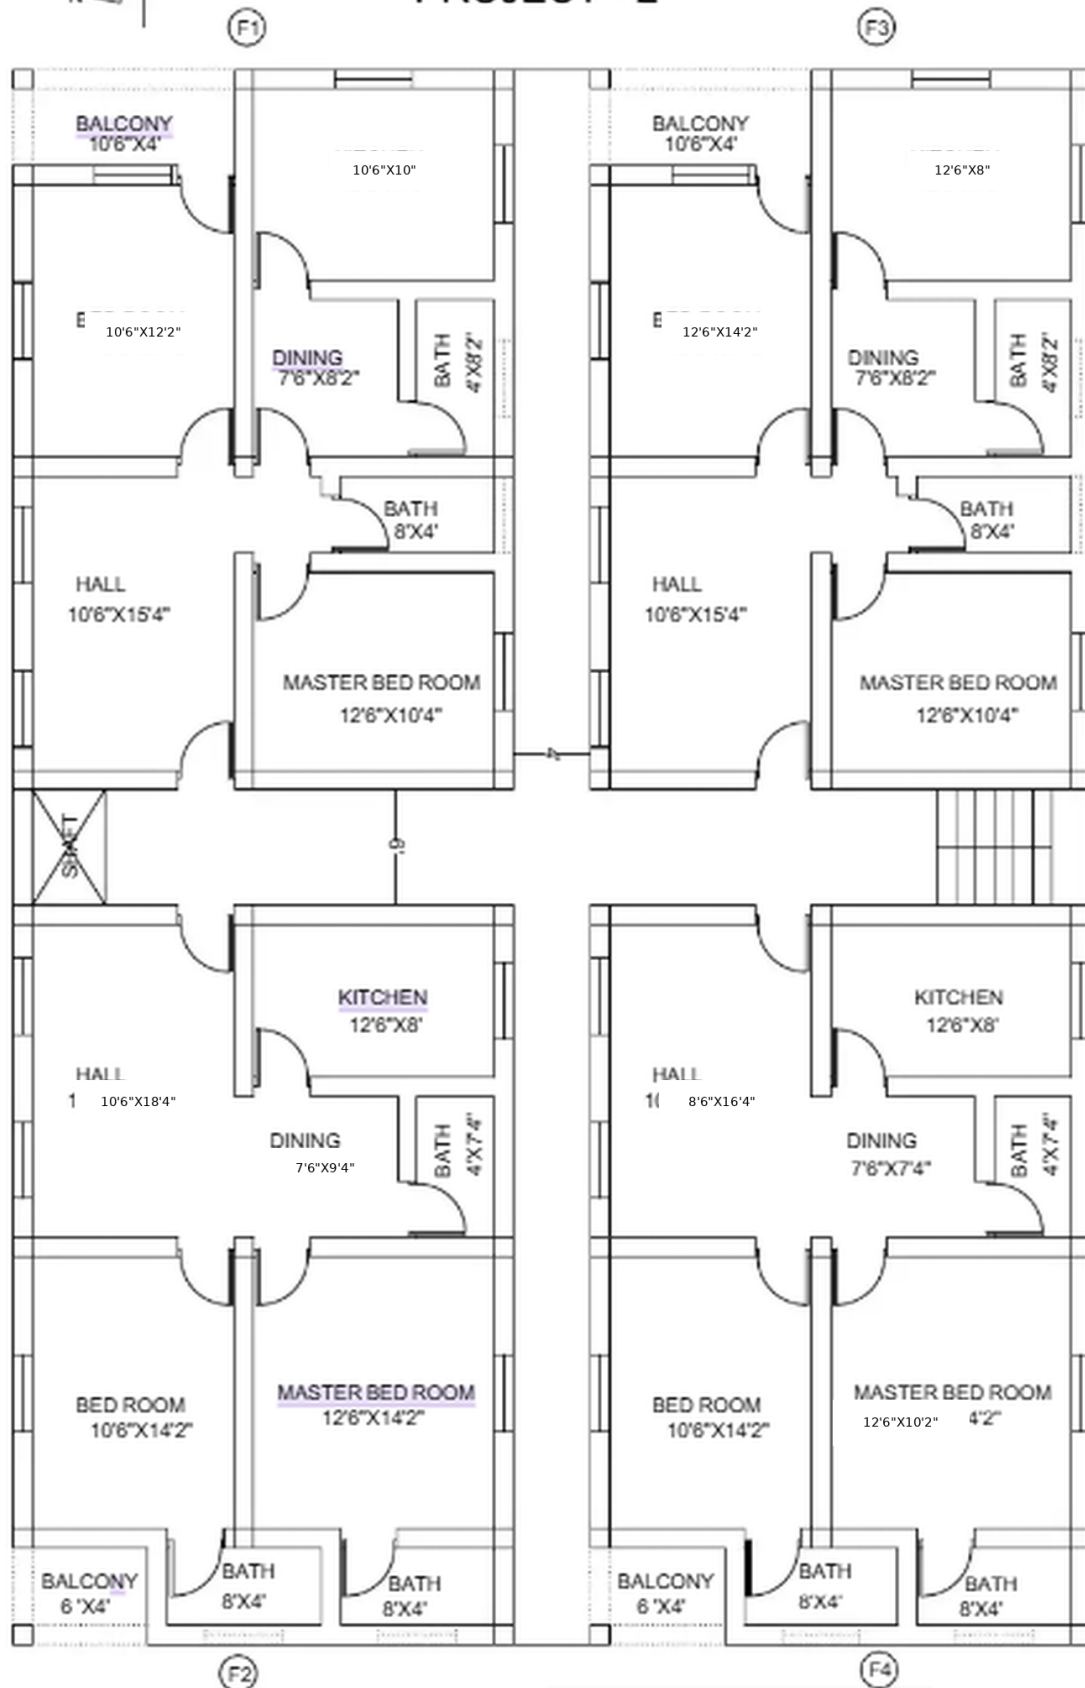

TYPICAL 1st, 2nd, 3rd, 4th, 5th FLOOR PLAN
GROUND FLOOR OPEN FOR PARKING (NON A/C)
HEIGHT 12', BOFC 10'4"

Dhanush Engg. Services India Pvt Ltd
www.meptrainings.com
www.mepjobsindia.com

